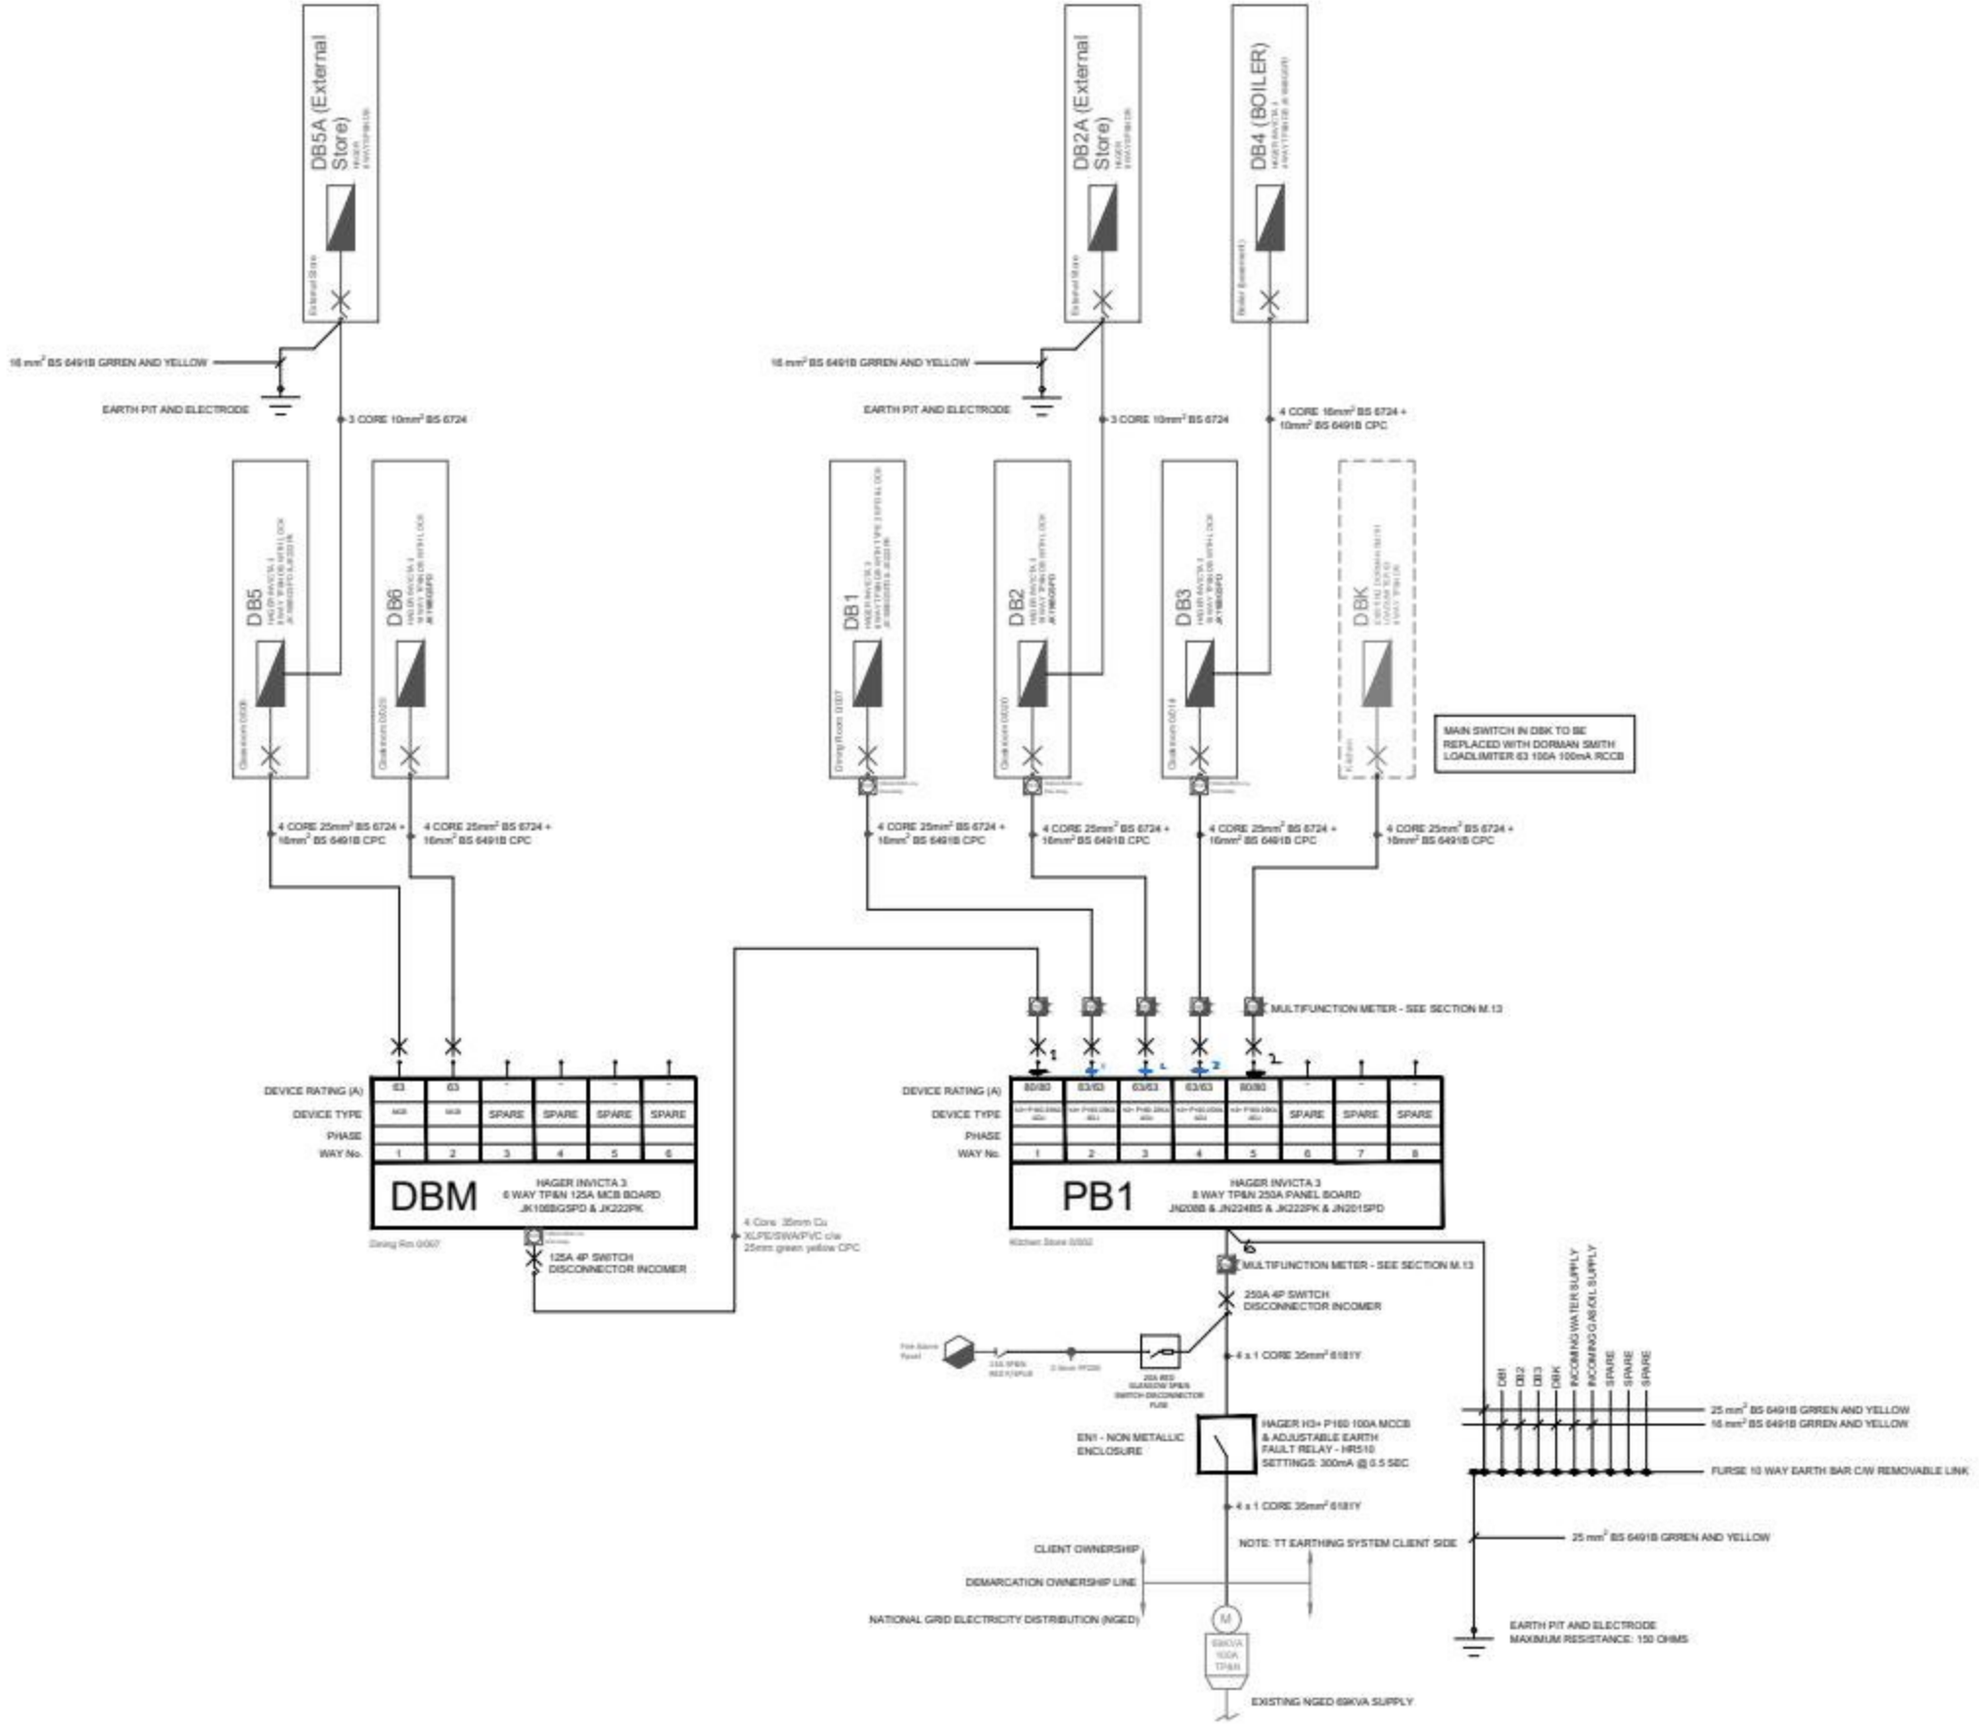


bullock consulting • certification

Client: Cyngor Sir Gâr Carmarthenshire County Council

PROJECT TITLE
TUMBLE CP
HEOL-Y-NEUADD,
TUMBLE, LLANELLI
SA14 6HR
REWIRE

DRAWING TITLE
PROPOSED DISTRIBUTION SCHEMATIC
SHEET 1 OF 3

DATE	SCALE
APRIL 2026	NTS
DRAWN BY: NMR	CHECKED BY: RAB
DRAWING NO.: BC250847/E13	ISSUE: TENDER